


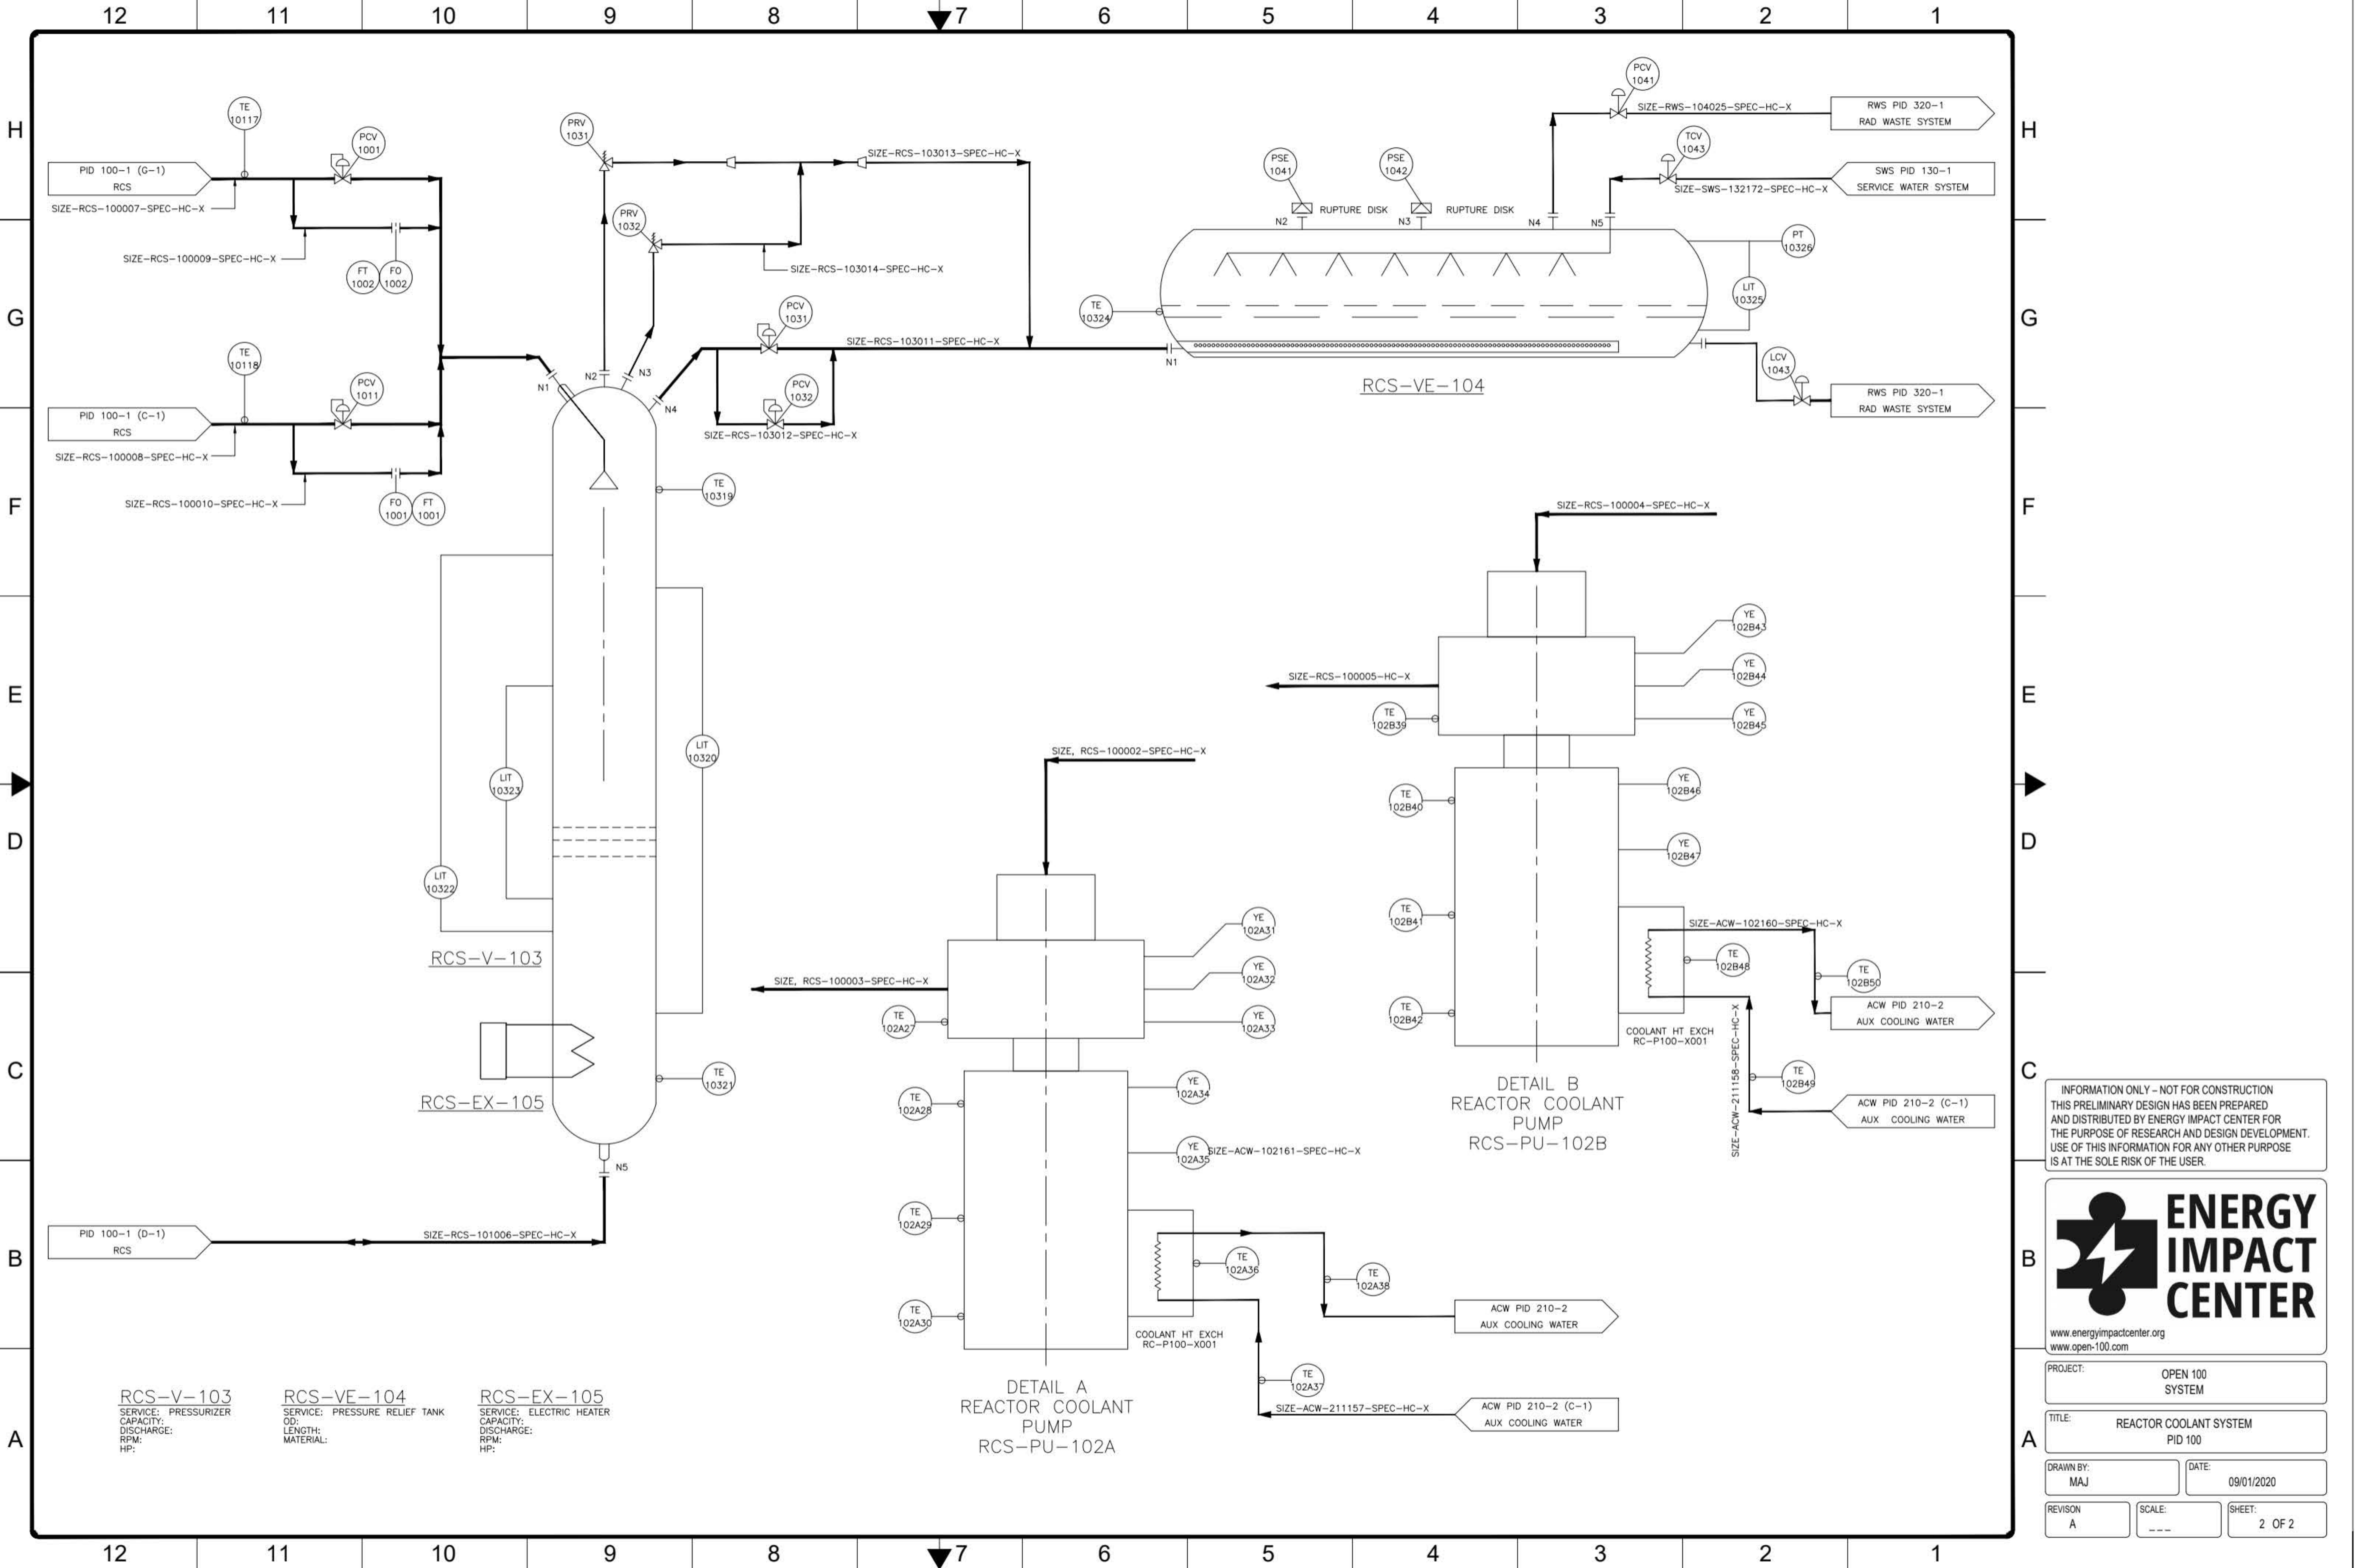

RCS-V-103
SERVICE: PRESSURIZER
CAPACITY:
DISCHARGE:
RPM:
HP:

RCS-VE-104
SERVICE: PRESSURE RELIEF TANK
OD:
LENGTH:
MATERIAL:

RCS-EX-105
SERVICE: ELECTRIC HEATER
CAPACITY:
DISCHARGE:
RPM:
HP:

DETAIL A
REACTOR COOLANT
PUMP
RCS-PU-102A

DETAIL B
REACTOR COOLANT
PUMP
RCS-PU-102B

INFORMATION ONLY - NOT FOR CONSTRUCTION
THIS PRELIMINARY DESIGN HAS BEEN PREPARED
AND DISTRIBUTED BY ENERGY IMPACT CENTER FOR
THE PURPOSE OF RESEARCH AND DESIGN DEVELOPMENT.
USE OF THIS INFORMATION FOR ANY OTHER PURPOSE
IS AT THE SOLE RISK OF THE USER.



PROJECT: OPEN 100 SYSTEM	
TITLE: REACTOR COOLANT SYSTEM PID 100	
DRAWN BY: MAJ	DATE: 09/01/2020
REVISION A	SHEET: 2 OF 2